

West



All plans & building work is subject to council approval. All dimensions & underground service locations to be checked prior to commencement of all works. DO NOT scale off drawings. Cross reference all drawings, confirm site levels, floor heights & restrictions prior to earthworks. If any discrepancies occur, ask the designer or contractor immediately before commencing works or ordering. COPYRIGHT ACD Architecture. All rights reserved. No part of this work covered by copyright may be re-produced or copied in any form by any means without the written permission.

ACDARCHITECTURE

Client Name: Adrian Currie Site Address: Lot 266, The Lakes Tauranga

ELEVATIONS						New Design	Job Number: ACD-249	Sheet no :
Wind:	High	Date:	09.09.14	Drawn:	CT		0 11 (0=) = 4	
Earthq:	2	Revision:		Check:		Call (07) 541 3133		
Exposure:	С	T.A:		Scale:	1:100	into@a	acdarchitectu	re.com

Floor

Concrete floor (see notes & details) (see notes & details) Cladding

Selected 70series brick veneer - ensure cavity & weep holes are free from excess mortar

Roof

25° pitch. NZS Colorsteel Endura - metal tiles

Fascia & Spouting


ZR8 continuous c/steel fascia & spouting with c/steel ENDURA downpipe system


Sheet no :

01 _{of 03}

Joinery

Residential suite aluminum joinery

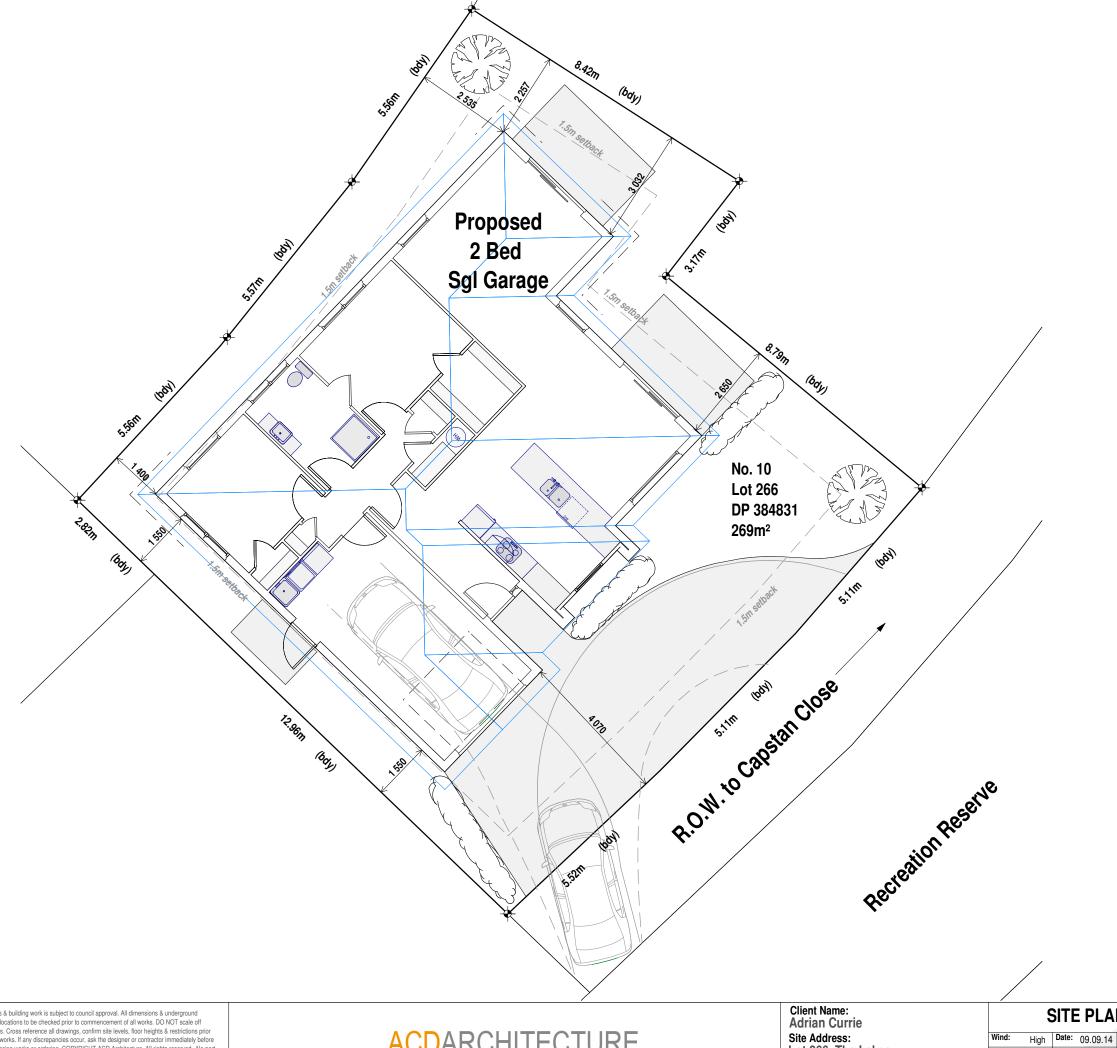

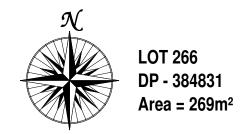



All plans & building work is subject to council approval. All dimensions & underground service locations to be checked prior to commencement of all works. DO NOT scale off drawings. Cross reference all drawings, confirm site levels, floor heights & restrictions prior to earthworks. If any discrepancies occur, ask the designer or contractor immediately before commencing works or ordering. COPYRIGHT ACD Architecture. All rights reserved. No part of this work covered by copyright may be re-produced or copied in any form by any means without the written permission.

ACDARCHITECTURE

Site Address: Lot 266, The Lakes Tauranga

Job Number: SITE PLAN New Design ACD-249
 Wind:
 High
 Date:
 09.09.14
 Drawn:
 CT

 Earthq:
 2
 Revision:
 Check:

Sheet no :

02
of 03 Call (07) 541 3133 Scale: 1:100 info@acdarchitecture.com Exposure: C T.A:



